



Согласовано		Взам. инб. №		Погр. и дата		Инб. № погр.	
ГП		АС					
АПС							

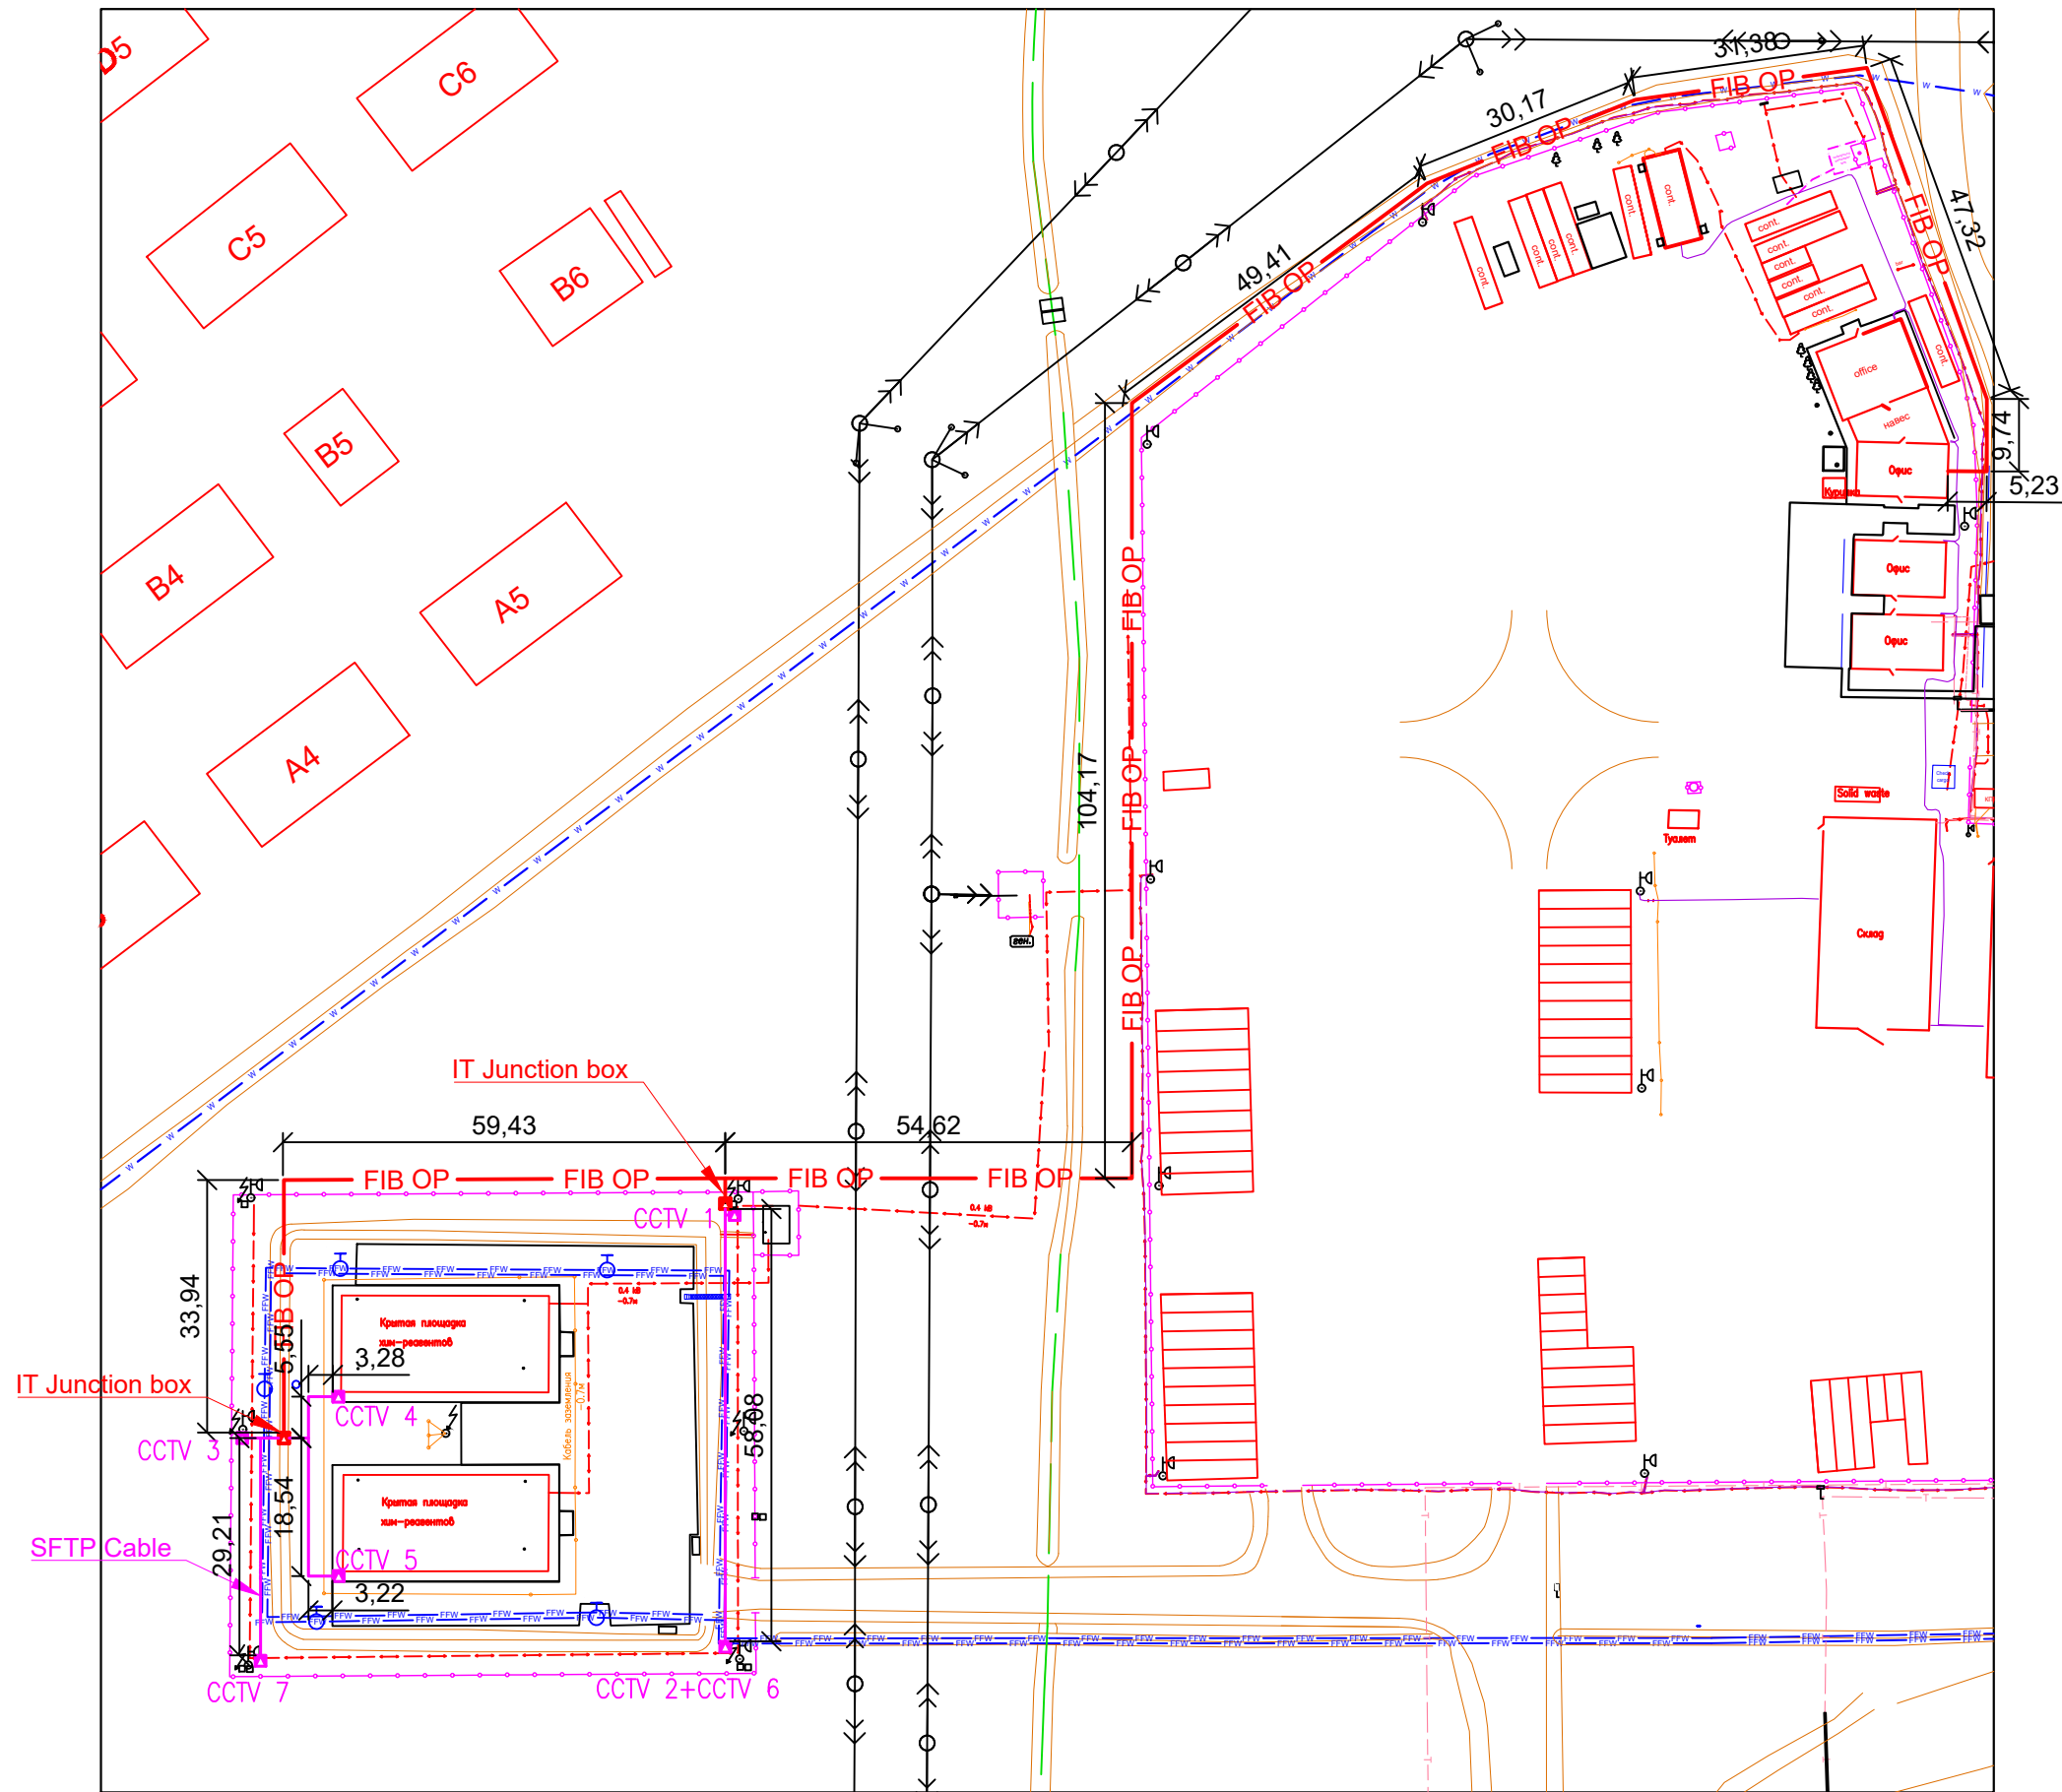


						*** ****			
Изм.	Кол.уч	Лист	№ док	Подпись	Дата	Система видеонаблюдения	Стадия	Лист	Листов
Разработал					**		РП	1	*
Проверил					**				
Н. контроль					**				
ГИП					**	6.2.1. Склад хим. Реагентов и Склад МСС	**** ***		

Согласовано		ГП	
		АС	АПС
Инф. № подл.		Погр. и дата	Взам. инф. №

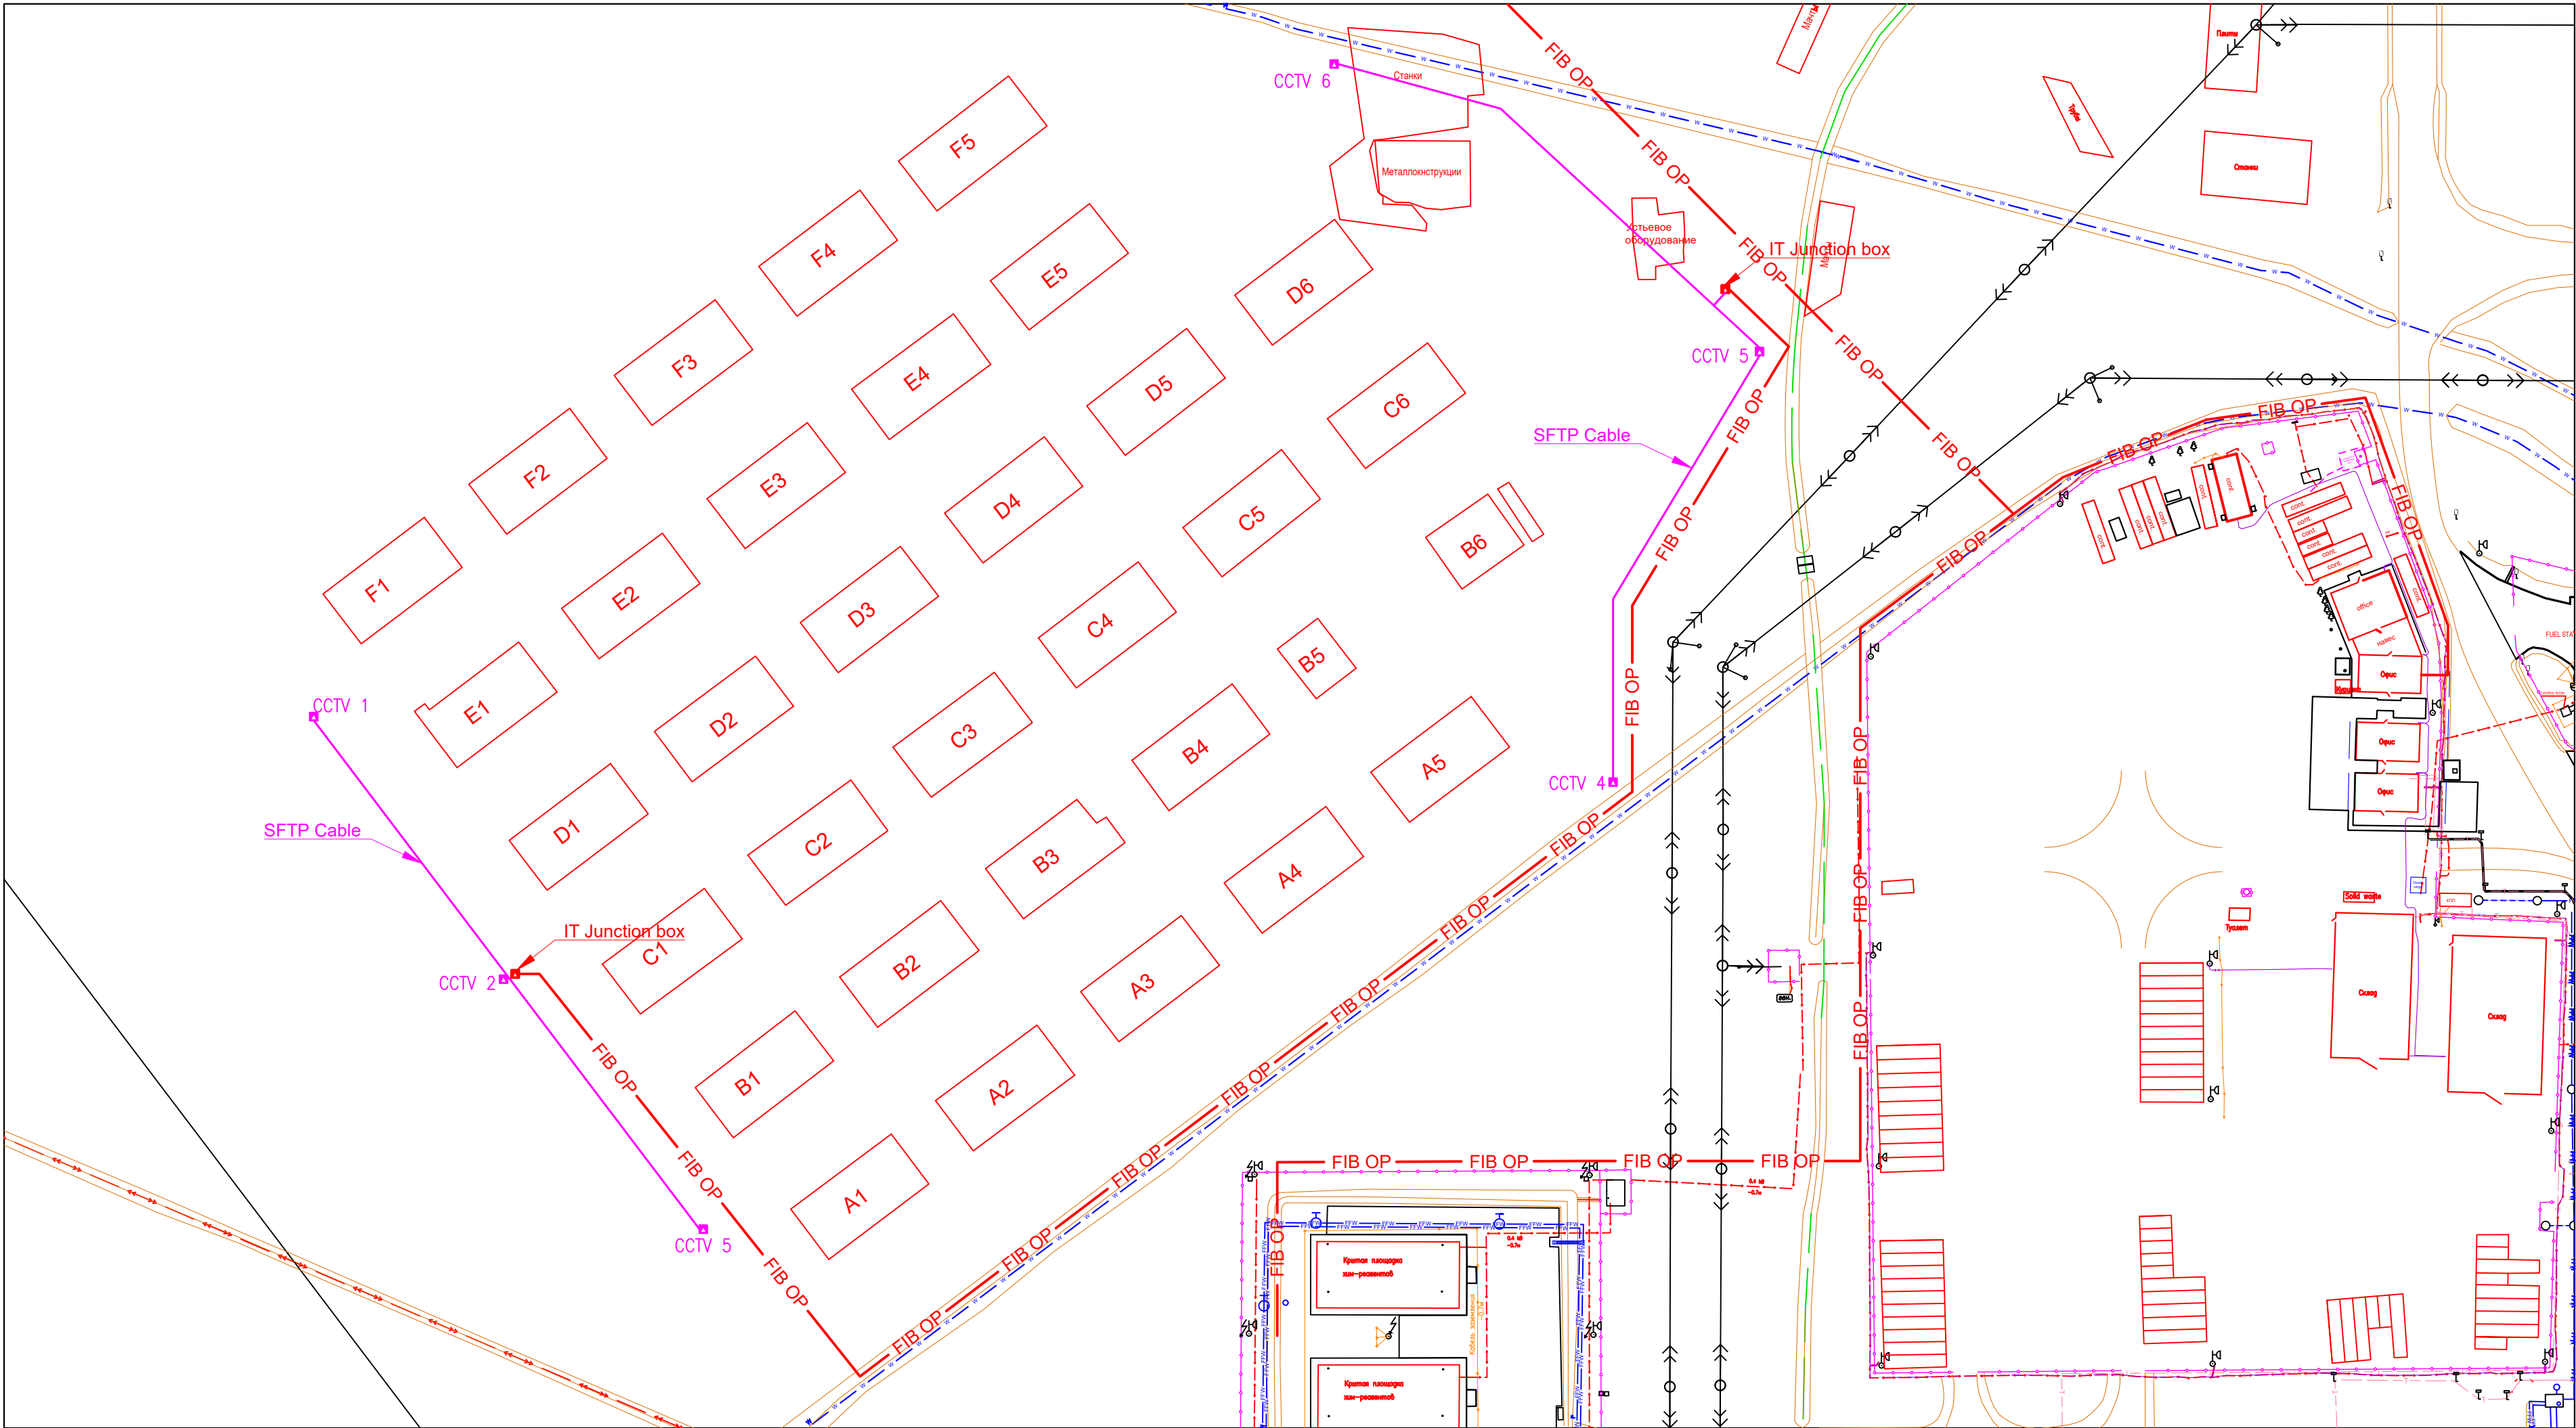


							*** ****
Изм.	Кол.уч.	Лист	№ док.	Погр. и дата			
Разработал				**		Система видеонаблюдения	Стадия
Проверил				**			РП
Н. контроль				**			Лист
ГИП				**			1
						Контейнерная площадка	Листов
							**** ***

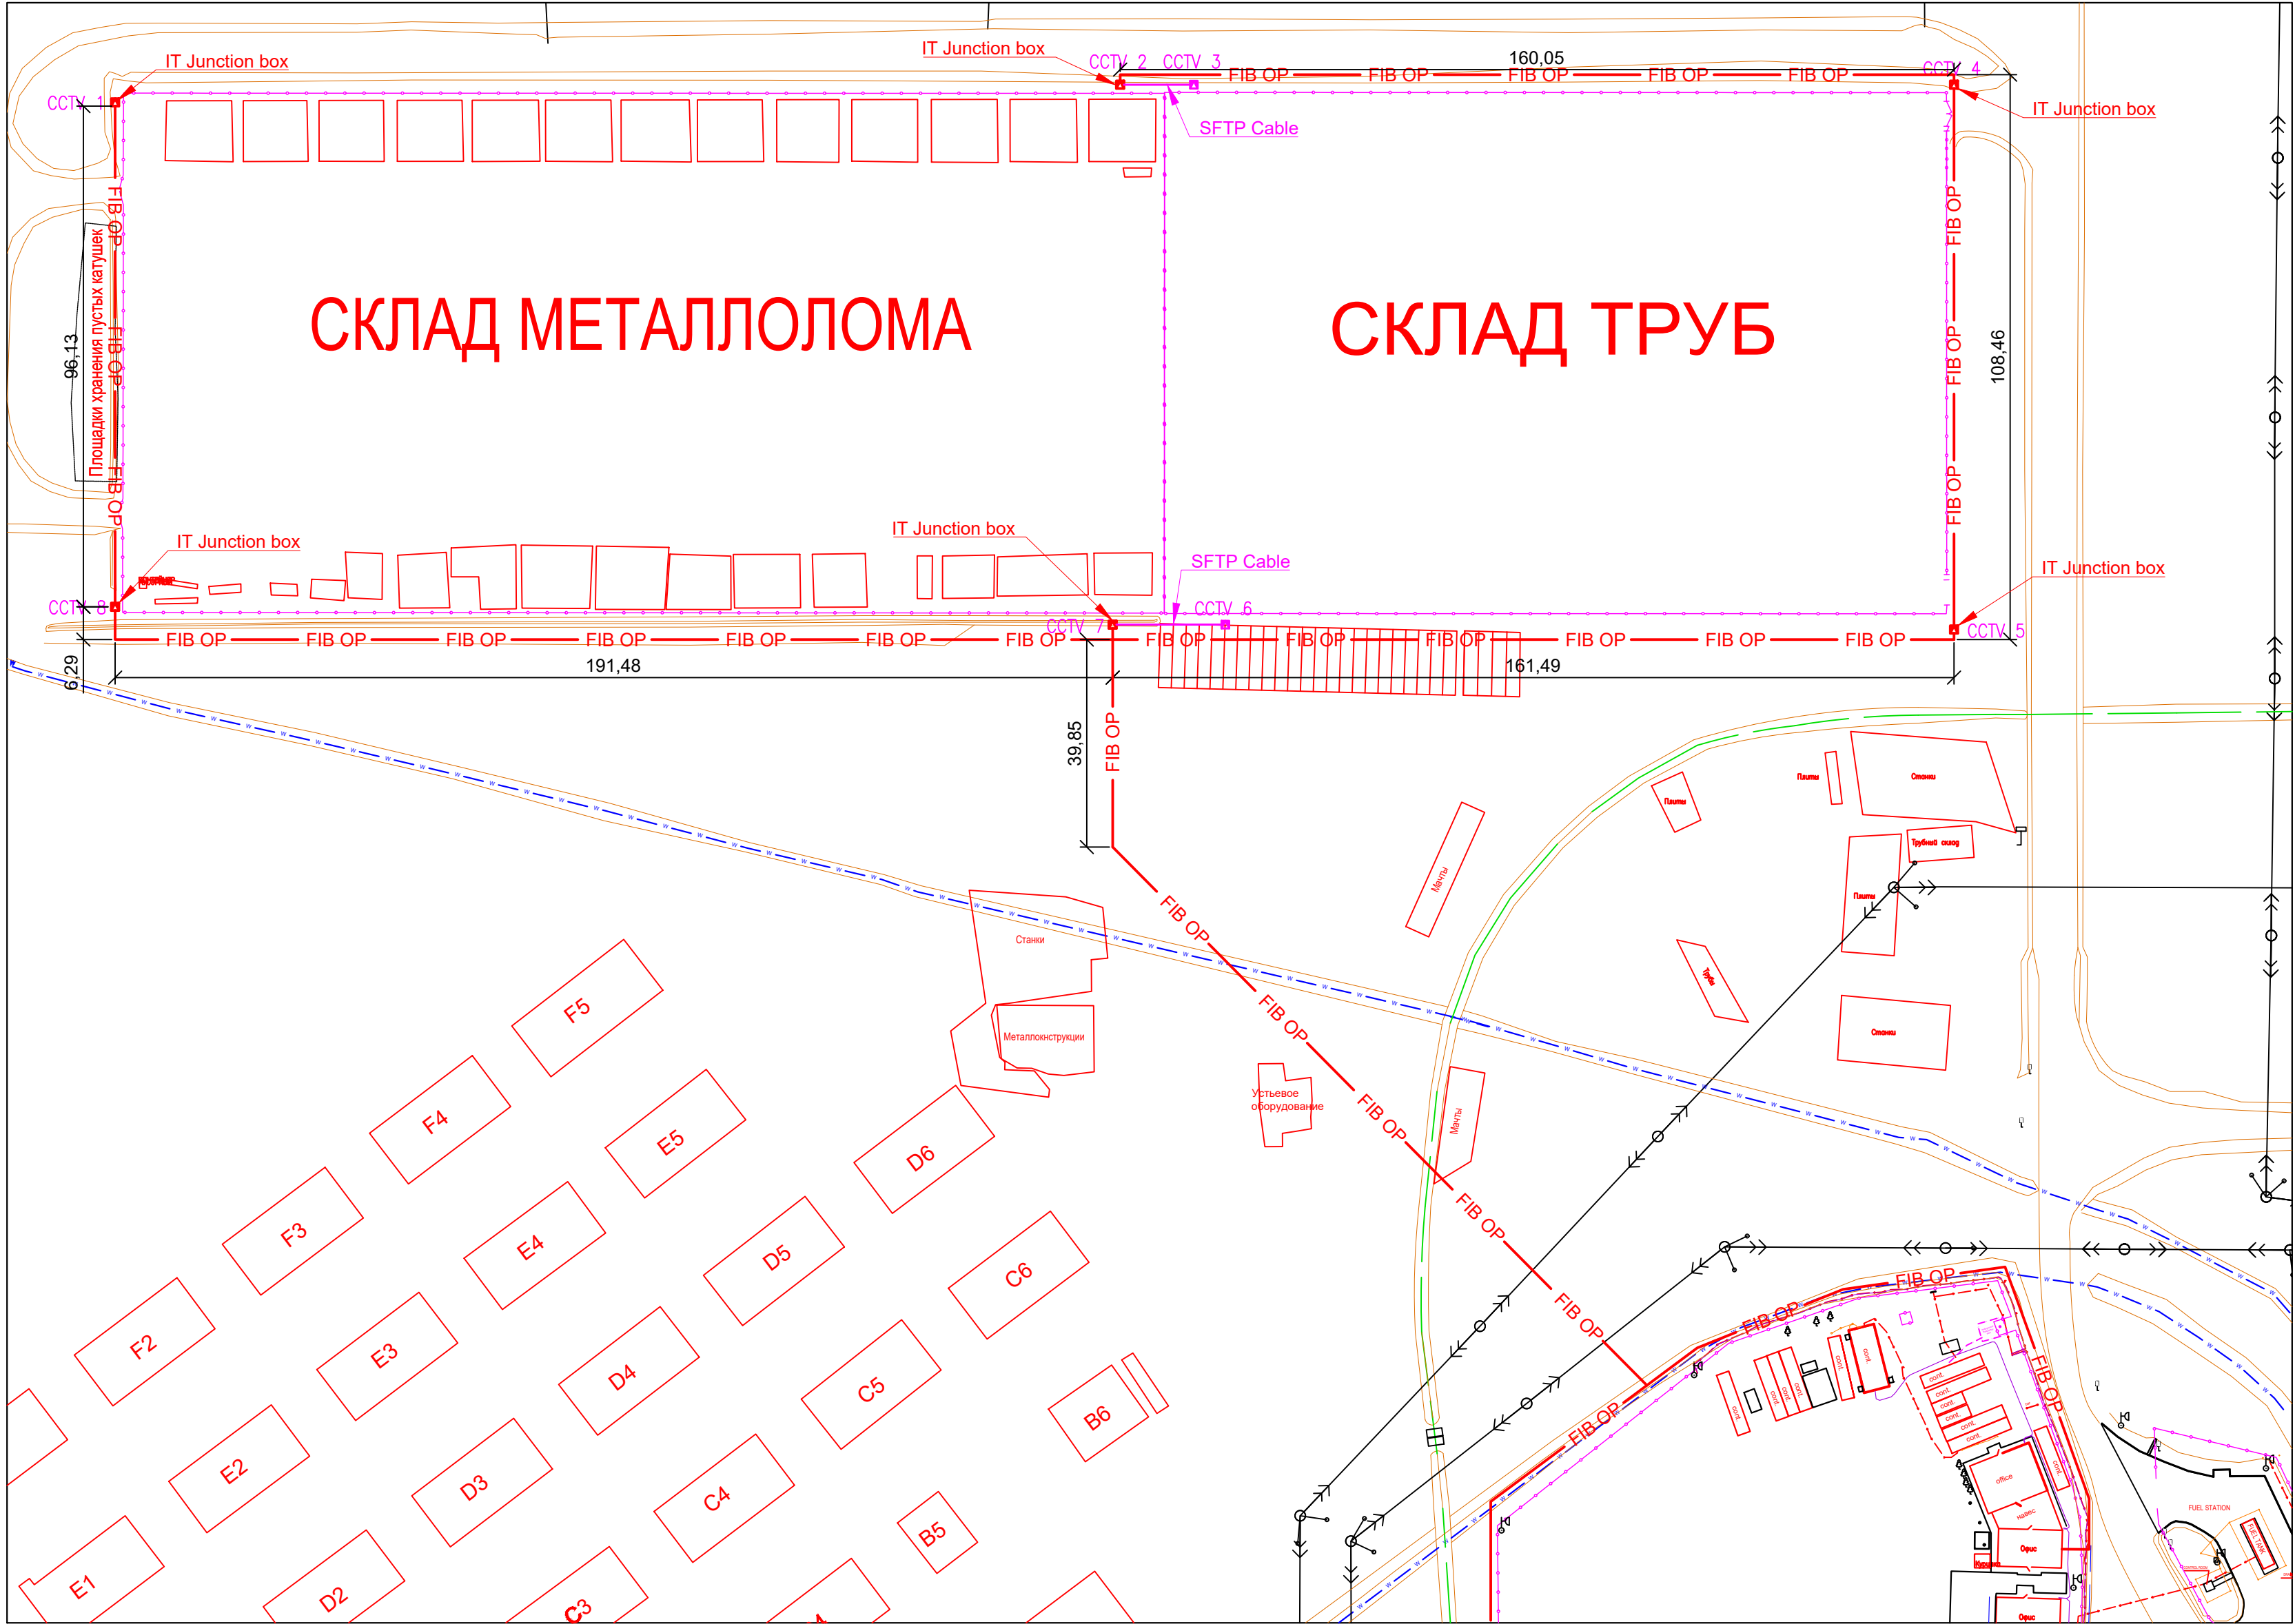

Согласовано		ГП	
		АС	
		АПС	
Инф. № подл.	Погр. и дата	Взам. инв. №	


							*** ****			
Изм.	Кол.уч.	Лист	№ док.	Погнись	Дата		Система видеонаблюдения	Стадия	Лист	Листов
Разработал					**			РП	1	*
Проверил					**					
Н. контроль					**		Трубная площадка 1	**** ***		
ГИП					**					

Согласовано			
ПП			
АС			
АПС			
Инф. № подл.		Взам. инф. №	
Погр. и дата			

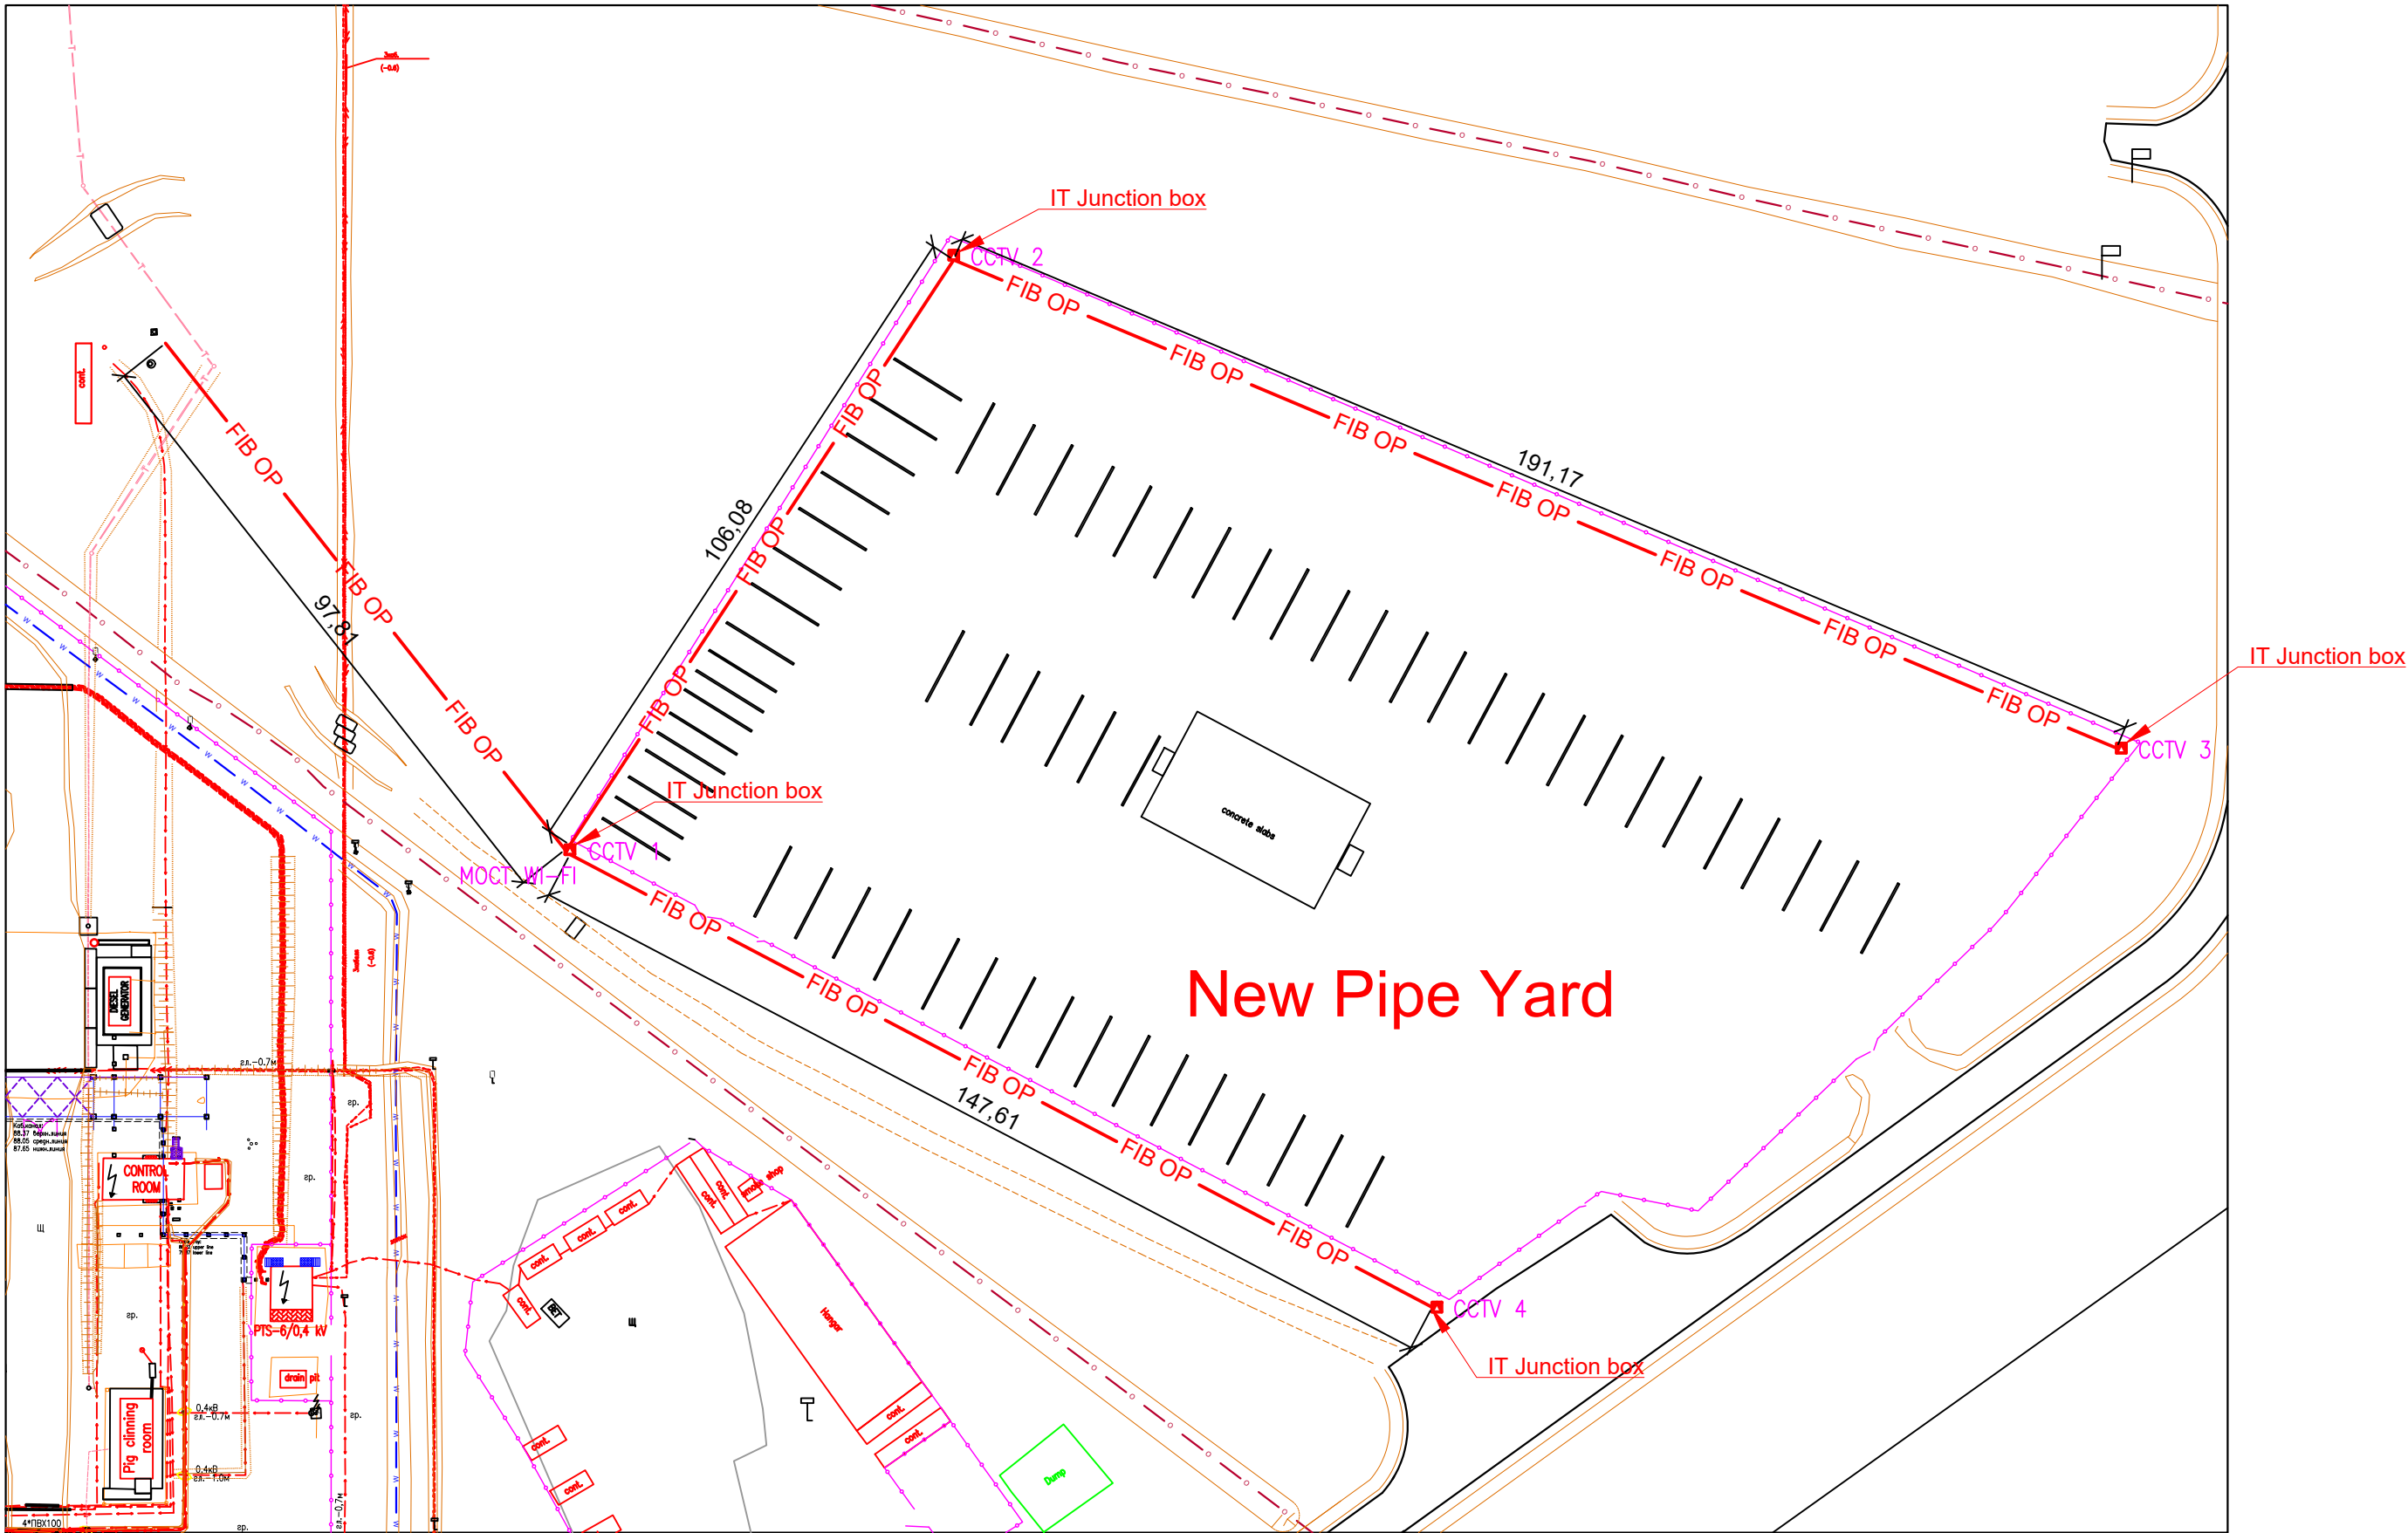

							*** ****
Изм.	Кол.уч.	Лист	№ док.	Погр. и дата			Система видеонаблюдения
Разработал				**			РП
Проверил				**			1
Н. контроль				**			*
ГИП				**			**** ***
							Трубная площадка 2
							**** ***

Согласовано		ГП			
		АС			
Инф. № подл.	Погр. и gamma		Взам. инф. №		

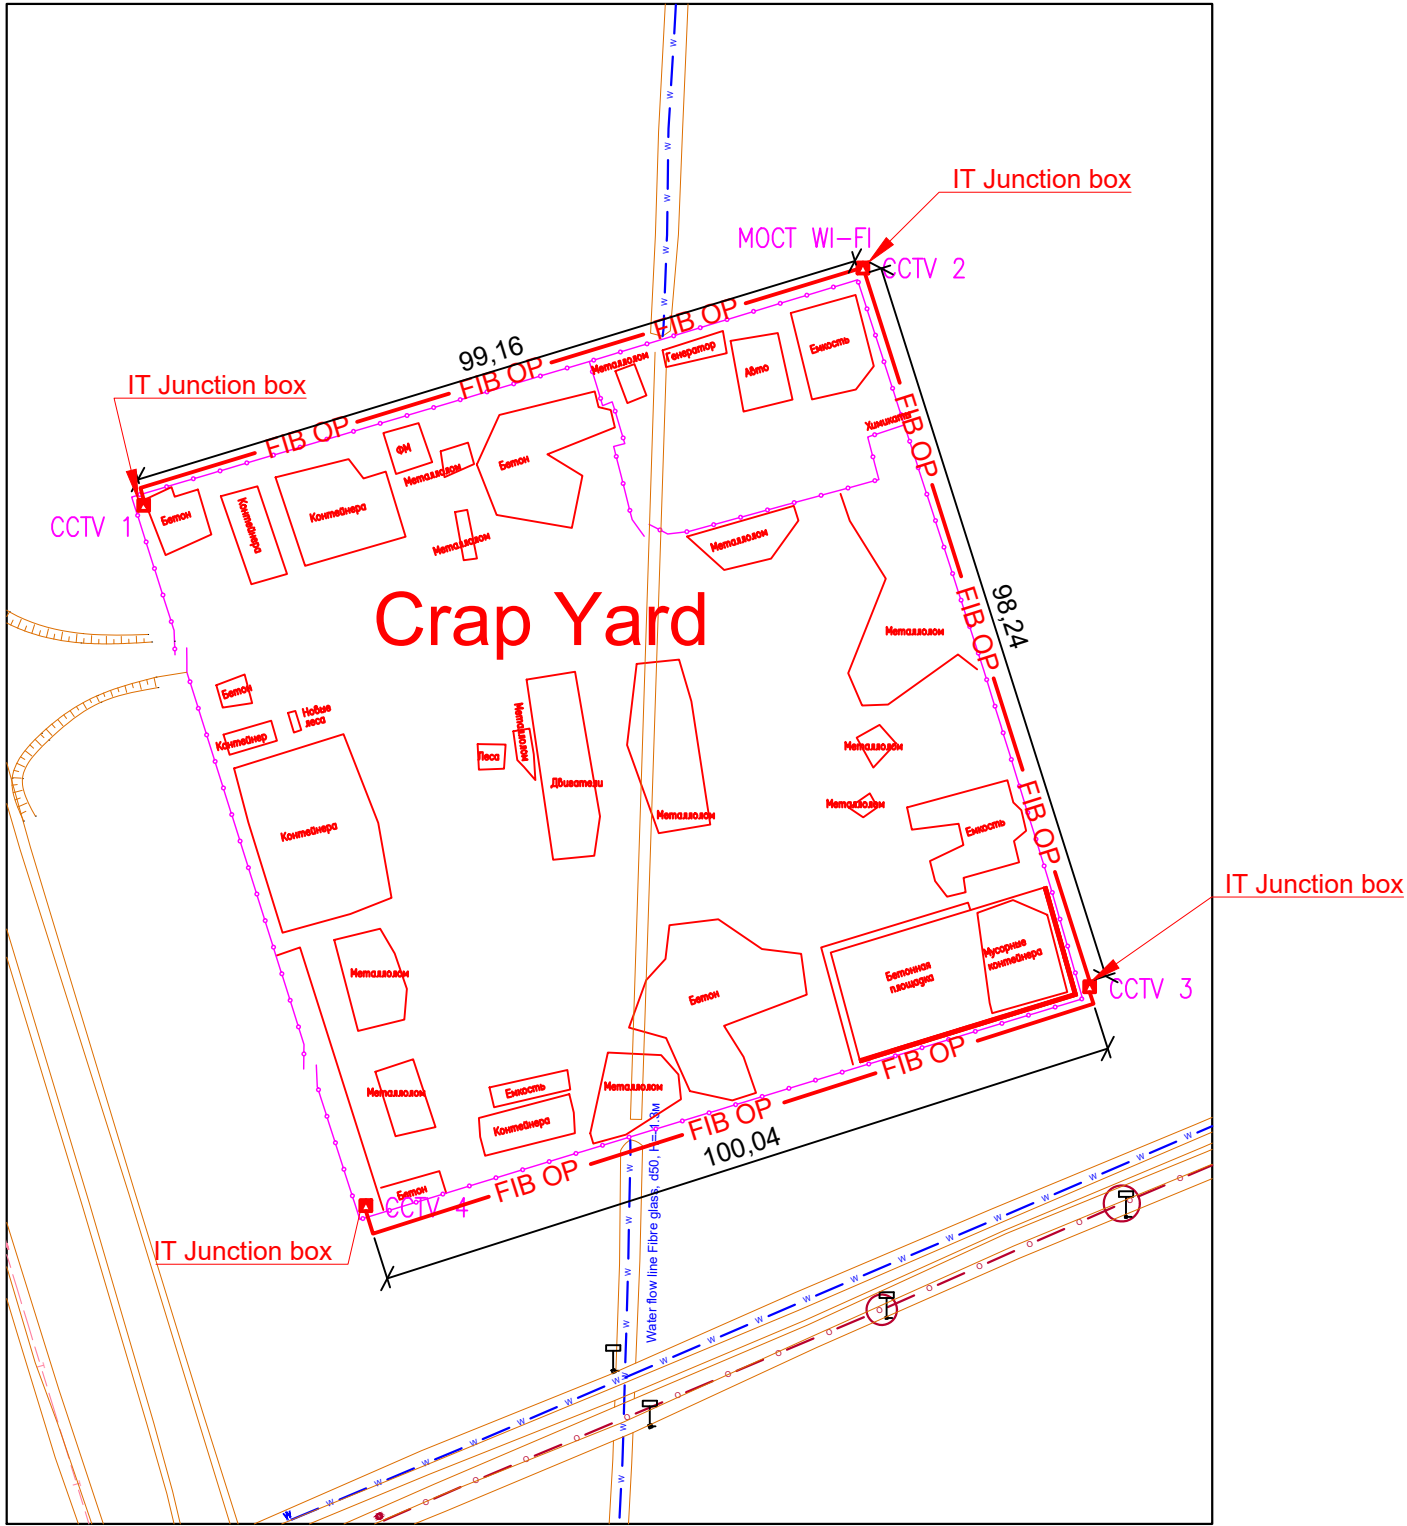

						*** ****			
Изм.	Кол.уч	Лист	№ док	Подпись	Дата				
Разработал					**	Система видеонаблюдения	Стадия	Лист	Листов
Проверил					**		РП	1	*
Н. контроль					**				
ГИП					**	Склад металлолома/ Склад отработанных материалов	**** ***		